




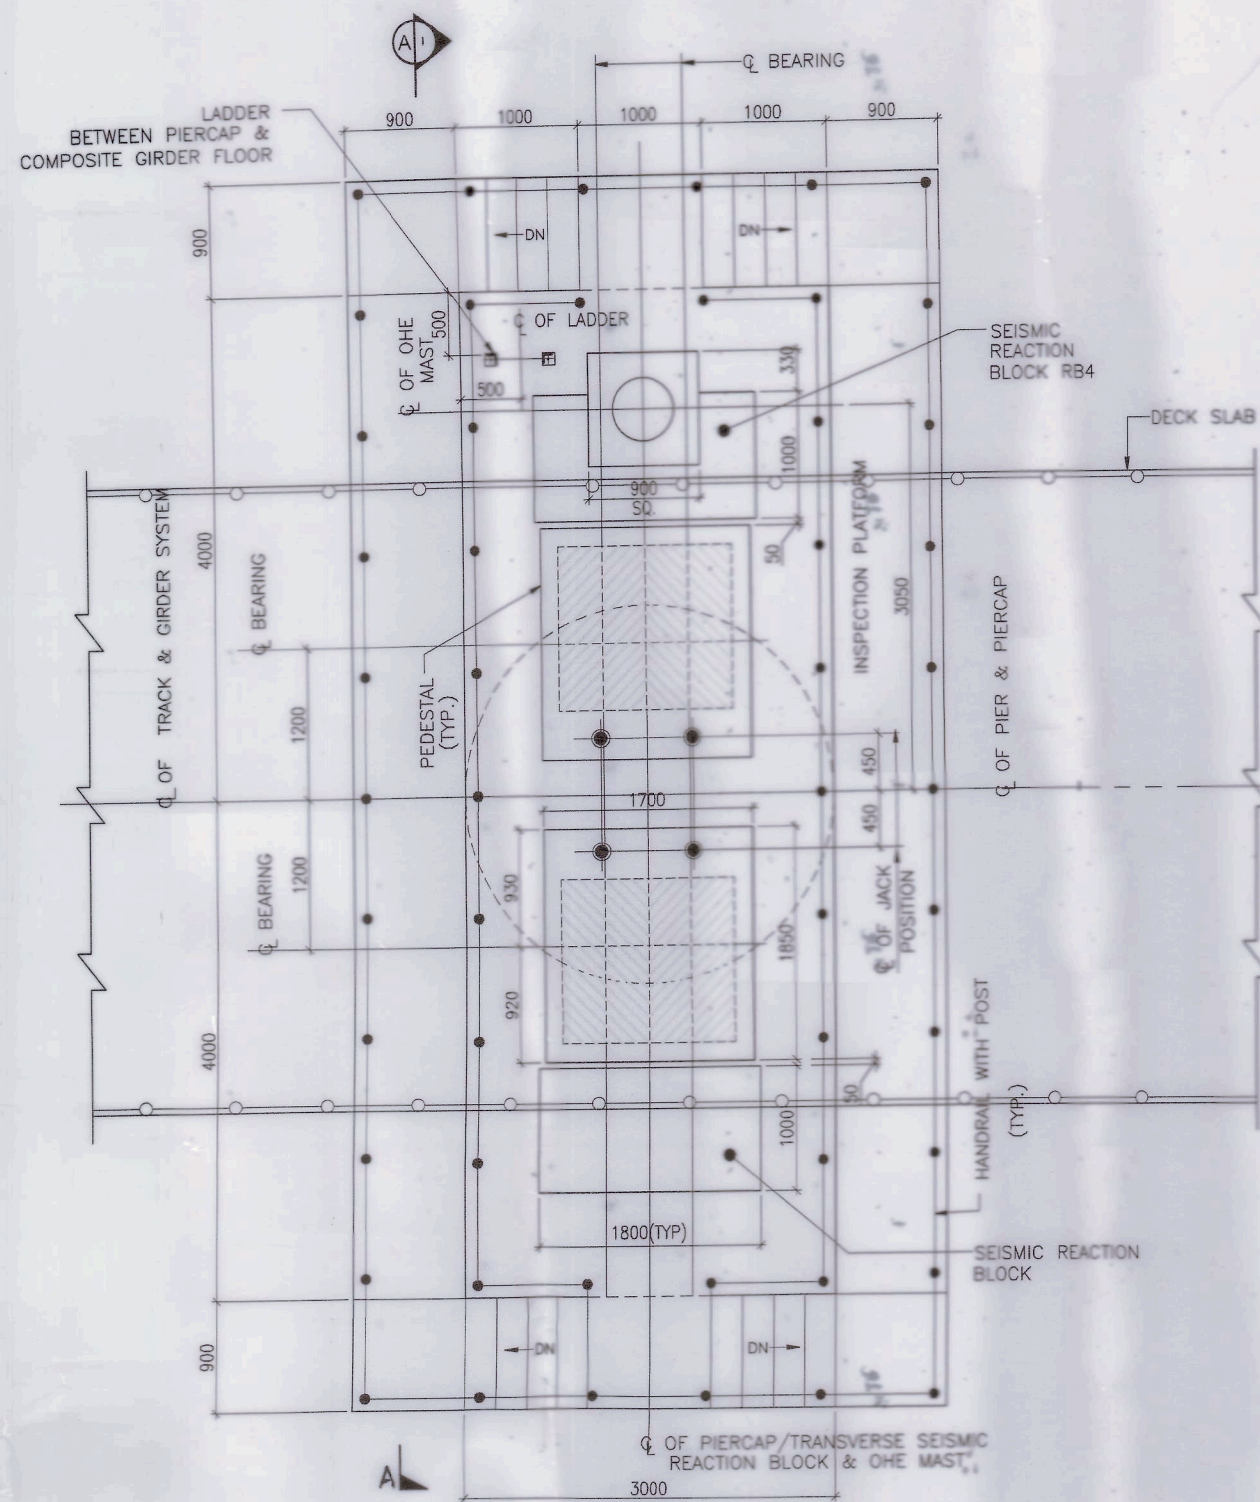

PLAN OF PIERCAP
(SCALE 1:40)

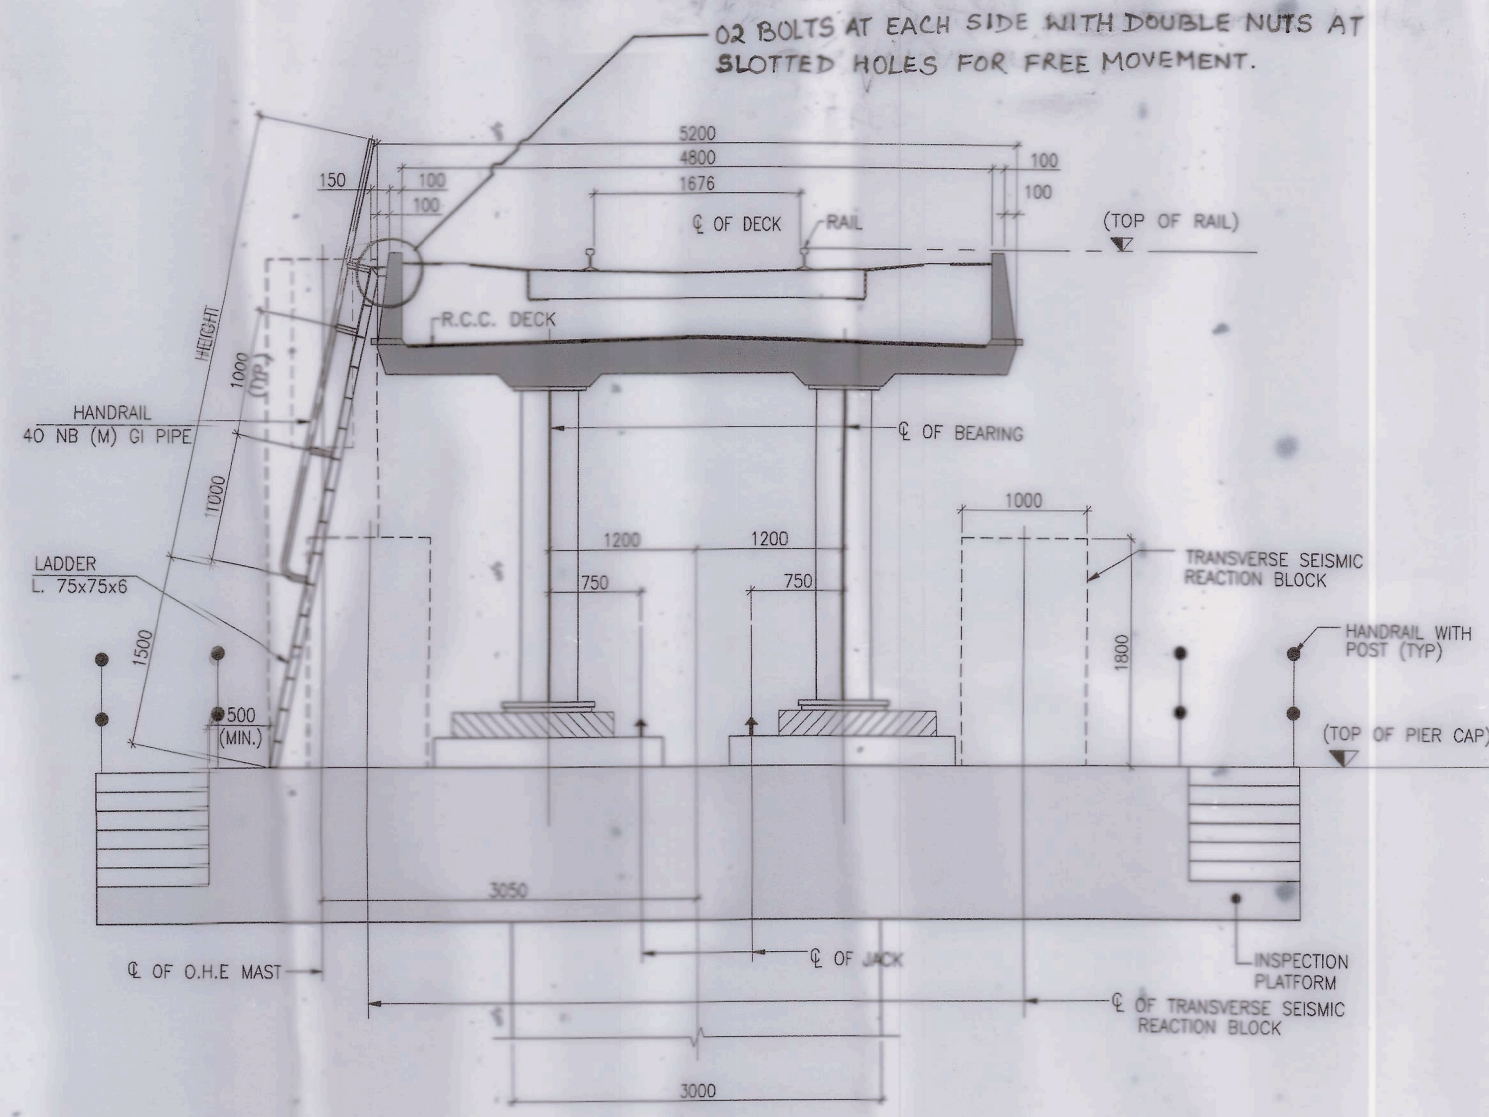


SECTION A-A
(SCALE 1:40)

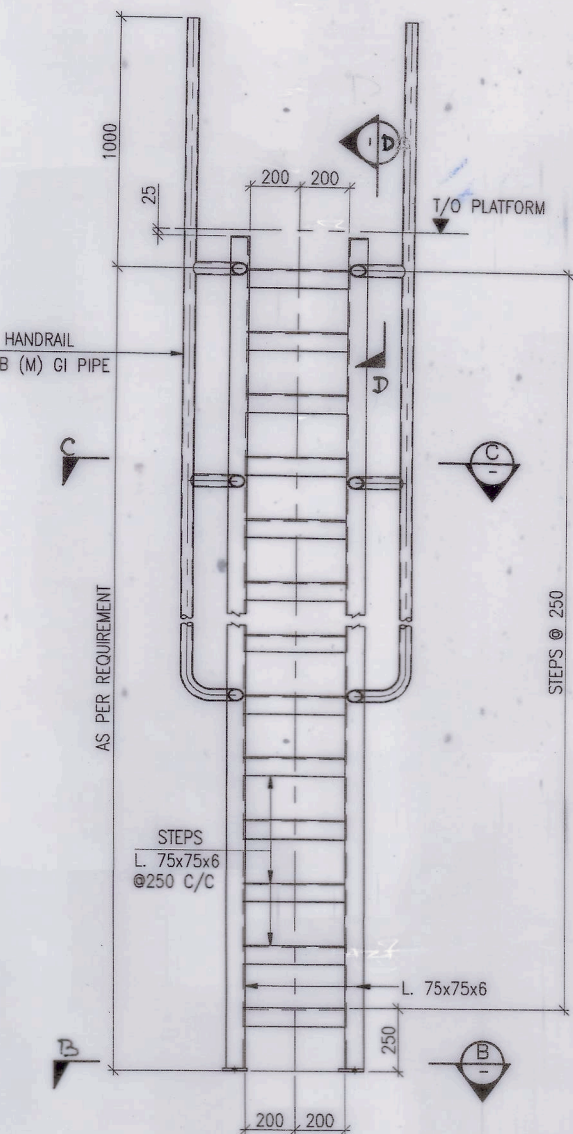


TYPICAL DETAIL OF LADDER
(SCALE 1:20)

NOTES :


1. ALL DIMENSIONS ARE IN MM AND LEVELS ARE IN METERS UNLESS NOTED OTHERWISE.
2. ALL STRUCTURAL STEEL SHALL CONFORM TO IS: 2062-2006 QUALITY "A" GRADE E250 (Fe 410W).
3. WELDING SHALL CONFORM TO IS: 816-1969.
4. ALL ELECTRODES SHALL CONFORM TO IS: 813-1986.
5. WELDING SYMBOLS ARE AS PER IS: 816-1961.
6. SIZE OF ALL FILLET WELDS SHOWN IN THE DRAWING ARE THROAT THICKNESS.
7. ALL STRUCTURAL STEEL SHALL BE TREATED WITH ONE COAT OF PRIMER FOLLOWED BY TWO COATS OF ALUMINUM PAINT.

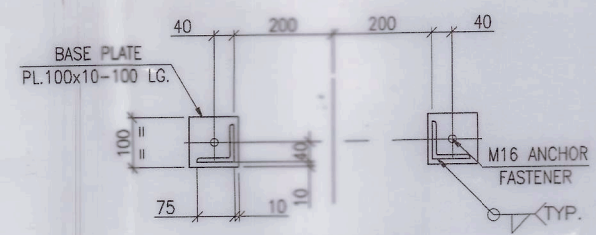


PLAN B-B
(SCALE 1:10)

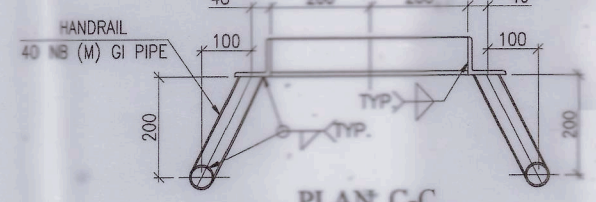

PLAN C-C
(SCALE 1:10)

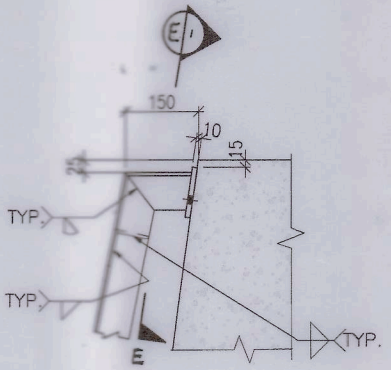

PLAN D-D
(SCALE 1:10)

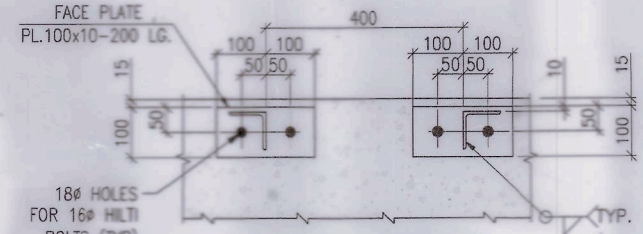

PLAN E-E
(SCALE 1:10)

PARIMAL KUMAR SSE/DRG/CAIZAWL N.F. RAILWAY	ASHIT DEBNATH Digitally signed by ASHIT DEBNATH Date: 2024.04.10 14:45:27 +05'30'	HARJIMA MEENA Digitally signed by HARJIMA MEENA Date: 2024.04.10 11:02:07 +05'30'	<i>[Signature]</i> SSE/CON/DRG N.F. RLY/MLG	<i>[Signature]</i> XEN/CON/DRG N.F. RLY/MLG	<i>[Signature]</i> DY/CE/CON/D-1 N.F. RLY/MLG	<i>[Signature]</i> CE/CON-2 N.F. RLY/MLG
--	---	---	---	---	---	--

DATE	No.	REVISION	DRAWN	CHECKED	APPROVED
OWNER			OFFICE OF ORIGIN		
NORTHEAST FRONTIER RAILWAY (CONSTRUCTION ORGANISATION)			KOLKATA		
DRG. NO. - CE/CON/MAJ/B-S/B/221/2024.			DATE		
			29.02.2024		
PROJECT			DRAWN		
PROPOSED BRIDGE NO. 194 & 195 (AT Km 48.467) IN CONNECTION WITH PROPOSED CONSTRUCTION OF NEW BG RAIL LINE IN BHAIRABI-SAIRANG SECTION OF N.F. RLY AT MIZORAM			<i>[Signature]</i> BK		
			CHECKED		
			<i>[Signature]</i> ABM		
TITLE			APPROVED		
GA & DETAIL OF LADDER BETWEEN PIER CAP & COMPOSITE GIRDER			<i>[Signature]</i> PMD SENIOR MANAGER (DESIGN)		
DRG. NO.: 9435/E/DD/194-195/SK-05			REV.		
			0		
THIS DRAWING IS THE PROPERTY OF STUP CONSULTANTS PVT. LIMITED. IT SHOULD NOT BE USED, COPIED OR REPRODUCED WITHOUT THEIR WRITTEN PERMISSION.			SCALE		
			AS NOTED		