


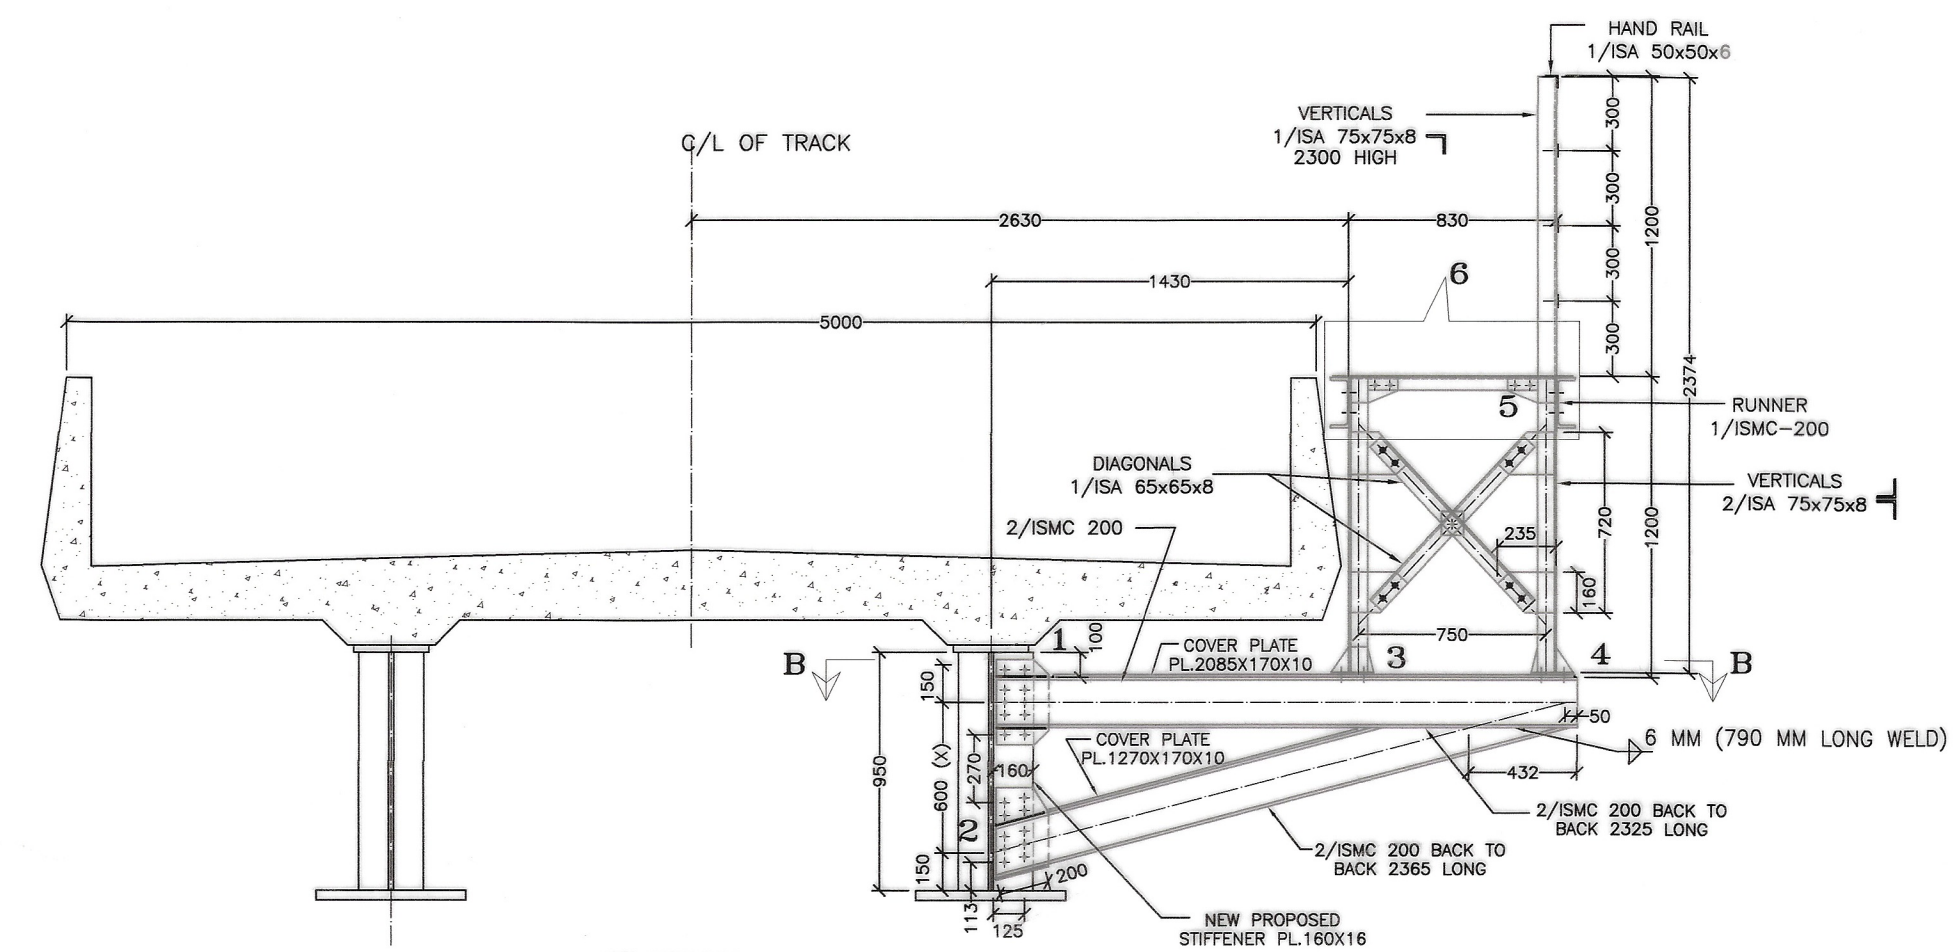

DETAILS AT '6'
(SCALE - 1:10)

PLAN E-E
(SCALE-1:10)

6 mm THK. CHEQD PLATE

VERTICAL
1/ISA 75x75x8

VERTICAL
2/ISA 75x75x8

RUNNER
1/ISMC-200

90

60

60


Technical drawing of a vertical plate assembly. The drawing shows a cross-section of a structure with a central vertical plate and two side plates. The central plate is labeled 'VERTICAL 1/ISA 75x75x8'. The side plates are labeled 'VERTICAL 2/ISA 75x75x8'. A horizontal plate at the top is labeled '6 mm THK. CHEQD PLATE'. A horizontal plate at the bottom is labeled 'RUNNER 1/ISMC-200'. Dimensions are indicated: a total width of 90, and two vertical segments of 60 each. The drawing is a technical sketch with lines and labels.

Diagram illustrating the Plan View of the Bridge Deck. The overall width is 1430 units. The deck is supported by two verticals, each 75x75x8 units. The deck thickness is 2325 units. The reinforcement consists of 2/10M20 bars (top and bottom) and 2/10M20 bars (verticals). The deck is covered with a 2/10M20 plate. The distance between the verticals is 830 units. The distance from the centerline to the edge of the deck is 750 units.


PLAN B-B
(SCALE - 1:30)

[illegible]


DETAILS AT '1'
(SCALE-1:10)

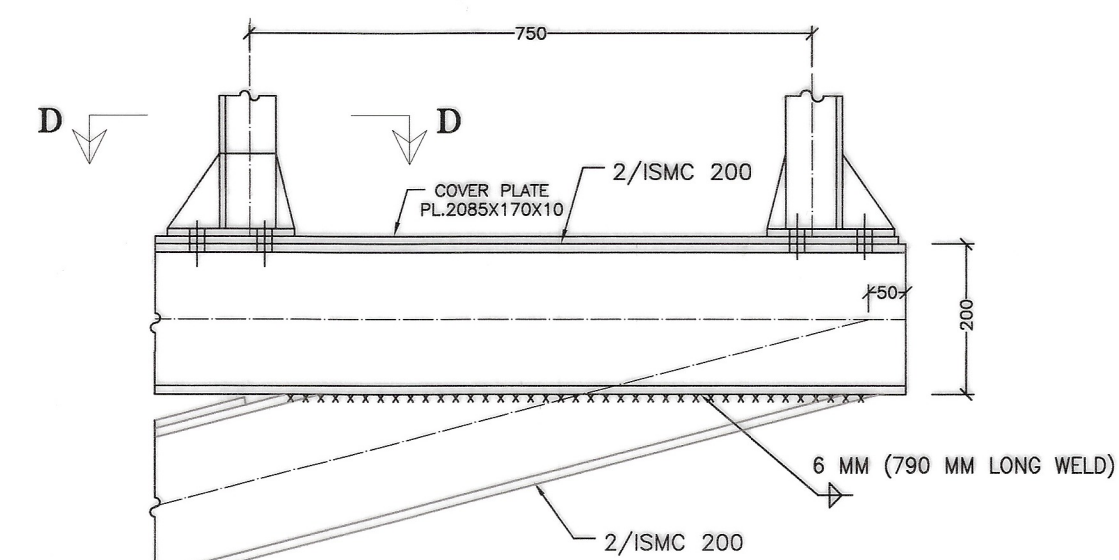


DETAILS AT '3' & '4'
(SCALE-1:10)

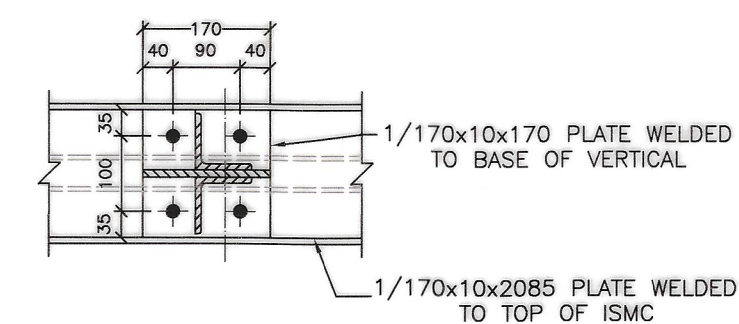

PLAN D-D (SCALE-1:10)

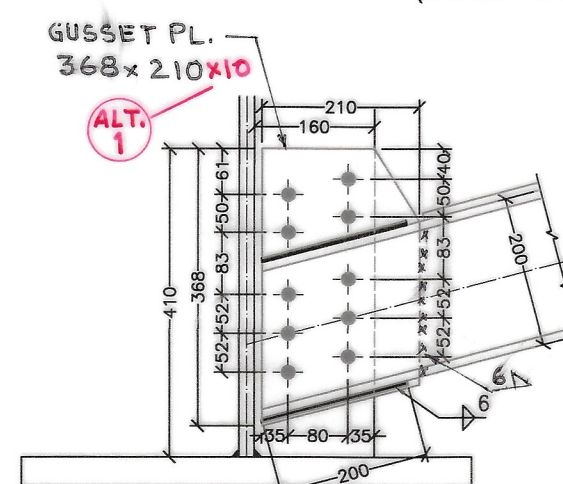


DETAILS AT '2'
(SCALE-1:10)

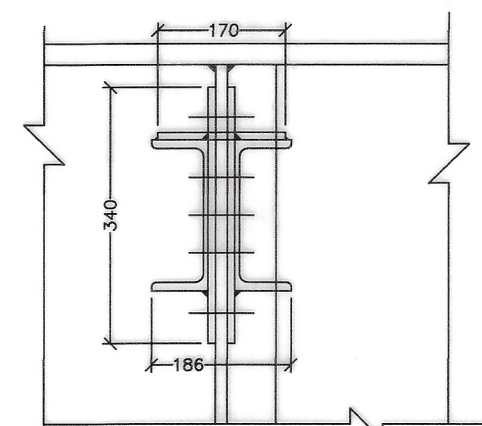

VIEW AT C-C
(SCALE-1:10)

- (SIZE-A1)
MILLIMETERS

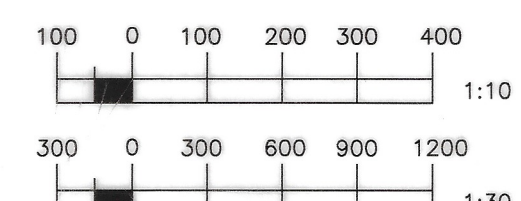

1 GUSSET THICKNESS AND
NOTE ADDED

यह आईएम अनुसन्धान अभिकल्प एवं मानक संगठन (रेल मंत्रालय) लखनऊ- २२६०११ (भारत) की संपत्ति है तथा बिना पूर्व लिखित अनुमति के इसका इस्तेमाल नहीं होना चाहिए अथवा इसकी/इसके किसी भाग की प्रतिलिपि नहीं बनायी जानी चाहिए.

THIS DRAWING IS THE PROPERTY OF RESEARCH DESIGNS & STANDARDS ORGANISATION (MINISTRY OF RAILWAYS) LUCKNOW-226011(INDIA) AND SHALL NOT BE USED, COPIED OR REPRODUCED IN PART OR WHOLE WITHOUT PRIOR CONSENT IN WRITING.

अ. अ. मा. सं. R. D. S. O.

DATE- 01.01.2018

CBS-0046

रेखांकन—MOHD.AZHAR (S.S.E.) Mazhar

रेखांकन जांच-ANEET KUMAR (J.E.)
Anet Kumar

मिलान एंव जांच - M. K. Shukla
M. K. SHUKLA (ADE/SB-II) 01.01.2018

मिलान एवं जांच
PRADEEP KUMAR (JDBS/SB-II)

अनुमोदन -
A. K. DADARYA (EDBS)

ऑटो कैड फाइल सं - B-
नोटिफिकेशन सं -

न रजिस्टर सं. DD/2018/1
डिजाइन-ANEET KUMAR (J.E.) Anet Kumar
जांच-NILESH KUMAR (S.S.R.E.) N. N. N.